


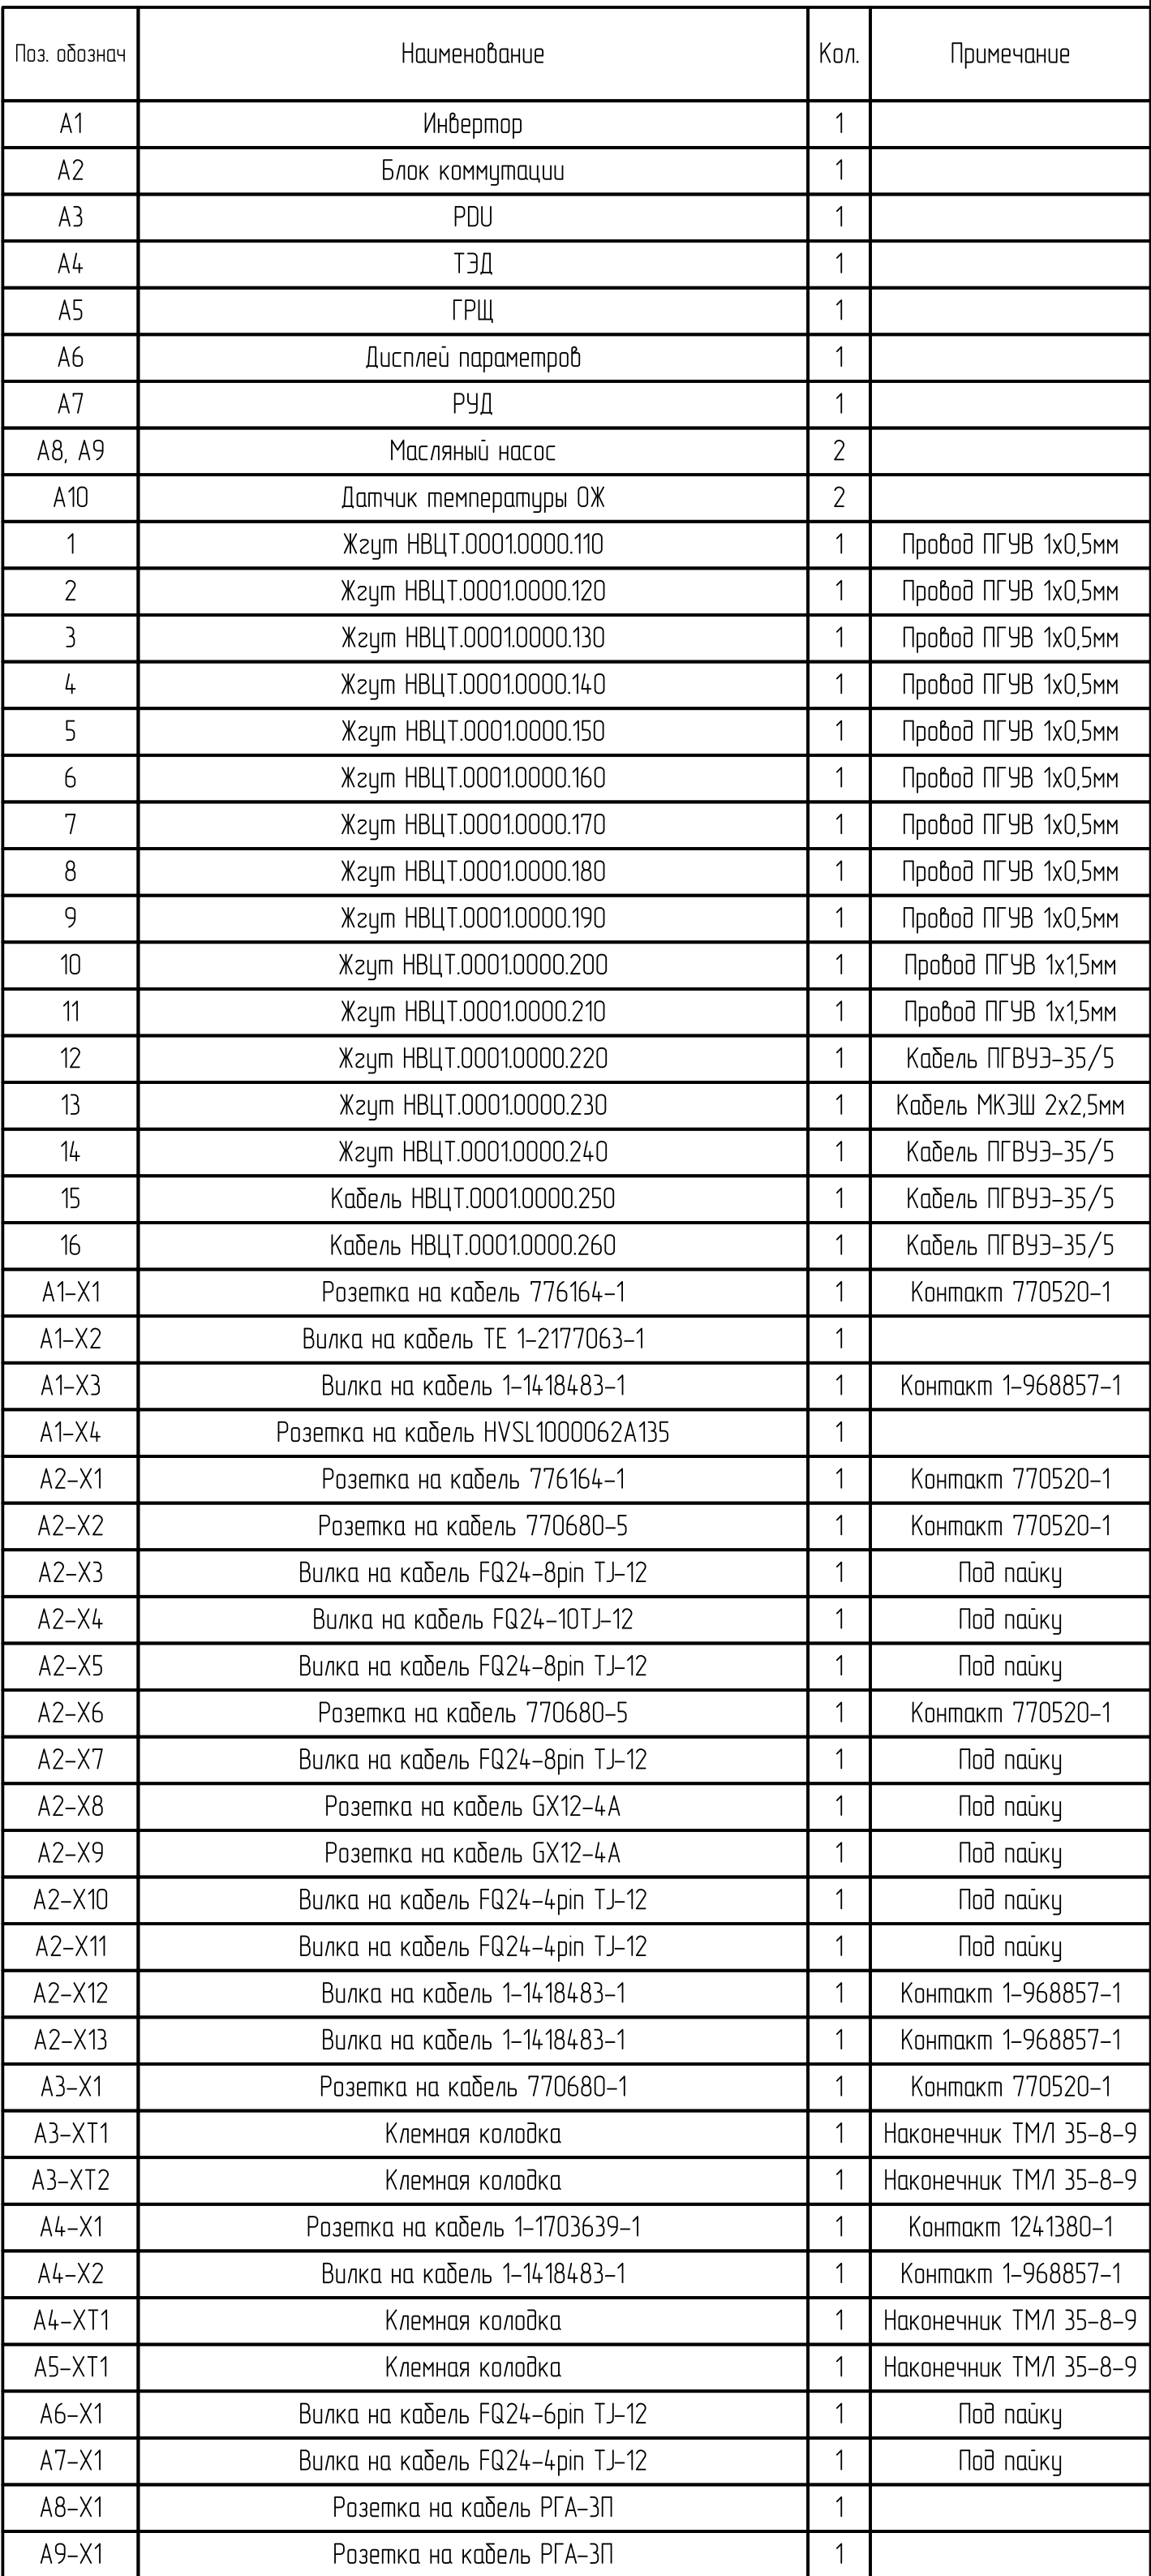

						650232.001 34				
						Система электродвижения Схема электрических соединений				
Иск.	Лист	№ докум.	Подп.	Дата		Лист	Масса	Масштаб		
Разраб.										
Проб.										
Т. контр.						Лист	1	Листов	1	
И. контр.						000 "Центр Водородных технологий"				
Утв.										